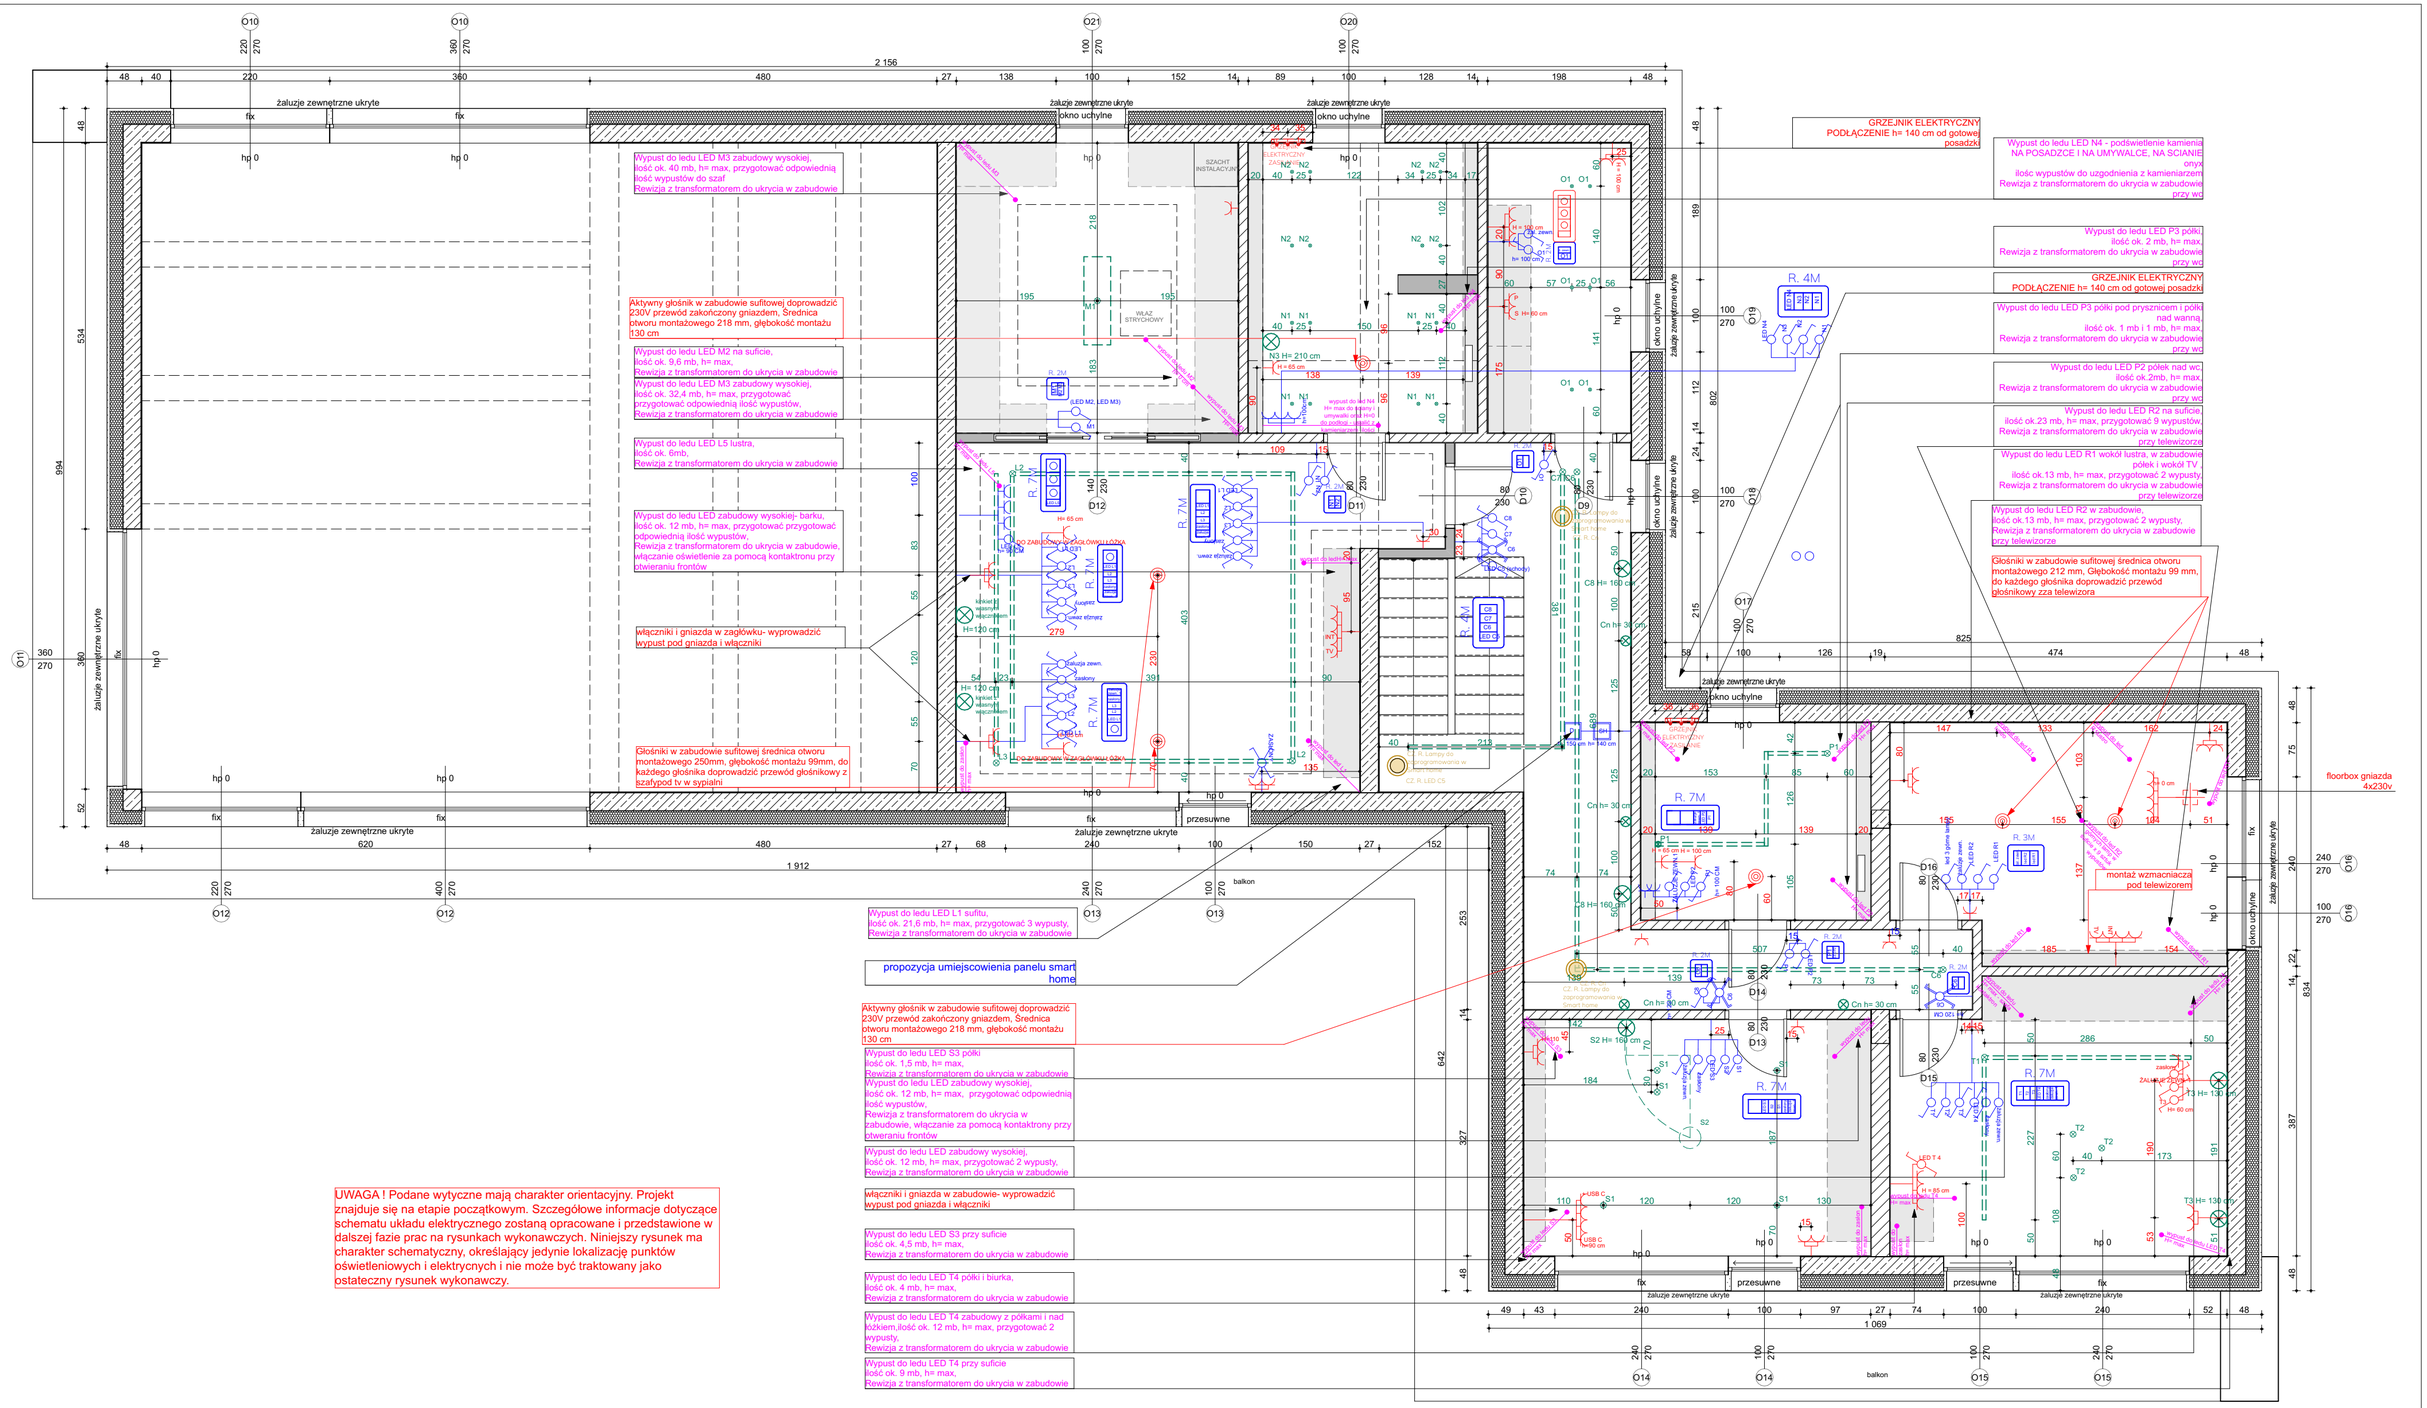

LEGENDA

- ramka pozioma
- gniazdo pojedyncze wtyczkowe h=23cm jeśli nie określono inaczej
- gniazdo pojedyncze wtyczkowe okap
- gniazdo pojedyncze wtyczkowe indukcja
- gniazdo pojedyncze wtyczkowe lodówka
- gniazdo pojedyncze wtyczkowe piekarnik
- gniazdo pojedyncze wtyczkowe zmywarka
- gniazdo pojedyncze wtyczkowe SERVO DRIVE
- gniazdo pojedyncze wtyczkowe pralka
- gniazdo pojedyncze wtyczkowe suszarka
- gniazdo pojedyncze RTV
- gniazdo pojedyncze internetowe
- wypust do zasilania led i inne
- wypust oświetleniowy sufitowy
- wypust oświetleniowy ścienny
- łącznik schodowy; H=1,2m chyba że określono inaczej
- łącznik jednobiegunowy; H=1,2m chyba że określono inaczej
- łącznik dwubiegunowy; H=1,2m chyba że określono inaczej
- łącznik schodowy podwójny;H=1,2M chyba że określono inaczej
- łącznik krzyżowy; H=1,2m chyba że określono inaczej
- domofon
- panel elektryczny
- nagłośnienie
- panel smart home
- rewizje
- czujnik ruchu sufitowy

Przyjęto ilość wypustów zasilania dla taśm LED wypust na 9 mb. taśmy led
Ostateczna ilość i rozmieszczenie wypustów do decyzji elektryka, zgodnie z zastosowaną taśmą LED i zasilaniem

Lokalizacja wszystkich czujników ruchu do uzgodnienia z wykonawcą instalacji, w celu weryfikacji poprawności umiejscowienia oraz zapewnienia prawidłowego działania urządzeń

UWAGA !
OSPRZĘT POD SYSTEM PUSZEK I RAMEK WŁOSKICH - WYMIARY RAMEK MOGĄ NIECO RÓŻNIĆ SIĘ OD STANDARDOWYCH - ODLEGŁOŚCI WŁĄCZNIKÓW I GNIAZD MOGĄ ULEC PRZESUNIĘCIU. WSZYSTKIE RAMKI MONTOWANE POZIOMO.

Osprzęt elektryczny Vimar Linea :
1. Ramka 2M :(9 X 8,8 CM) index code 30642.01
2. Ramka 3M : (12,28 X 8,8 CM)index code 30653.01
3. Ramka 4M (14,6 X 8,8 CM) : index code 30654.01
4. Ramka 7M : (20,85 X 8,8 CM): index code 30657.01

UWAGA: WSZYSTKIE WYMIARY PODANE DO OSI ŚRODKOWEJ PUSZKI. PRZED PRZYSTĄPIENIEM DO PRAC SPRAWDZIĆ WSZYSTKIE WYMIARY NA BUDOWIE.
WYKONAWCA MA OBOWIĄZEK ZAPOZNAĆ SIĘ Z KARTĄ TECH. OPRAWY PRZED PRZYSTĄPIENIEM DO PRAC.
UWAGA ! : WSZYSTKIE WYMIARY ŚCIAN I OTWORÓW DRZWIOWYCH PODANE SĄ NA GOTOWO Z POSADZKĄ I TYNKAMI ! PRZED PRZYSTĄPIENIEM DO PRAC SPRAWDZIĆ WSZYSTKIE WYMIARY NA BUDOWIE.

Rysunek chroniony w myśl przepisów ustawy z dnia 04.02.1994 o Prawie Autorskim i Prawach Pokrewnych, Dz.U. z 2000, Nr 80, poz. 904, ze zmianami.

UNDER studio	BIURO PROJEKTOWE	INWESTOR	TYTUŁ RYSUNKU	FAZA PROJEKTU	OPRACOWANIE	SKALA RYSUNKU	Nr arkusza
	UNDER STUDIO hello@understudio.pl 500366325	LIPIŃSCY	PIETRO WYTYCZNE DO WSTĘPNEGO SCHEMATU UKŁADU ELEKTRYCZNEGO	Koncepcja	Agnieszka Kułakowska Maria Trojnara Joanna Stawiak	1:100, 1:60 WYS. POMIESZCZEŃ OD 250/ 622 cm	9 Luty 2026