28.01.26

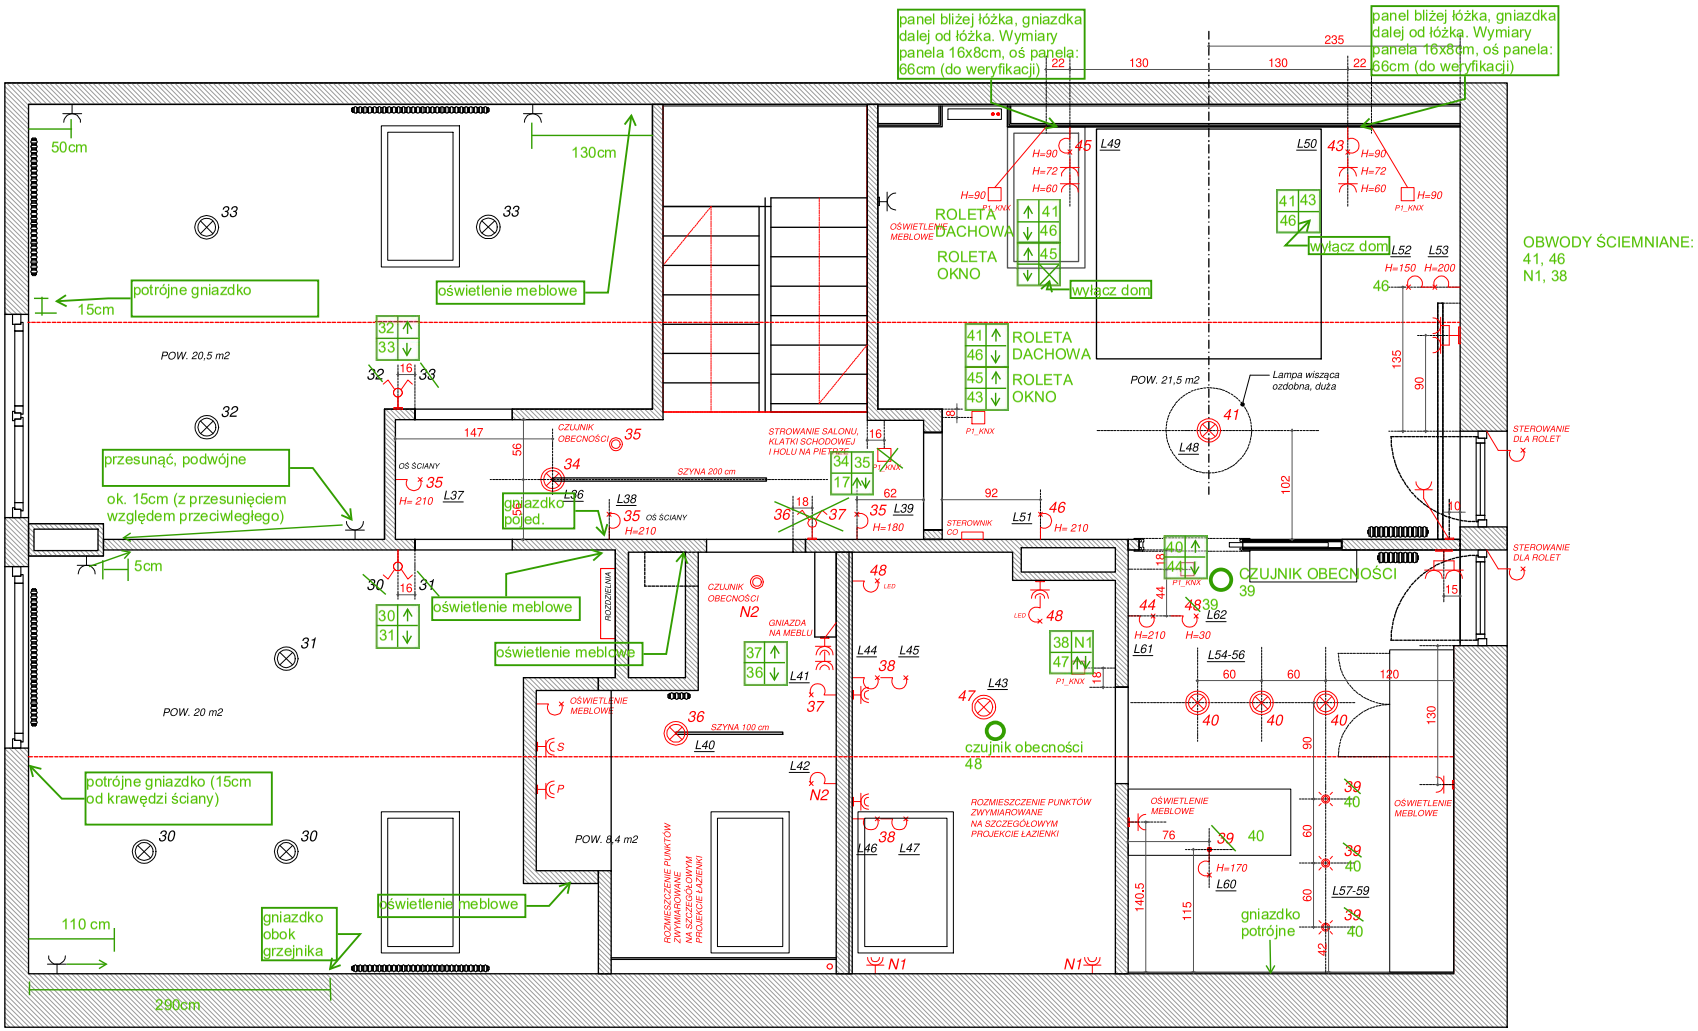

(!) WSZYSTKIE ŹRÓDŁA ŚWIATŁA W DOMU - BARWA 3000K

(!) WYMIARY NA RYSUNKU PODANO W CENTYMETRACH

(!) WYMIARY PODANO OD ŚCIAN TYNKOWANYCH

(!) ŁAZIENKI ROZPATRYWAĆ WG. PROJEKTÓW SZCZEGÓŁOWYCH

(!) WYSOKOŚĆ OPISANYCH PUNKTÓW ELEKTRYCZNYCH PODANO OD POZIOMU POSADZKI GOTOWEJ
GRUBOŚĆ POSADZKI 1,5 cm

GNIAZDA I ŁĄCZNIKI BEZ OPISANEJ WYSOKOŚCI MONTAŻU - MONTAŻ NA STANDARDOWEJ WYSOKOŚCI:
GNIAZDA H = 30
ŁĄCZNIKI H = 120

CZERWONYM KOLOREM ZAZNACZONE PUNKTY ELEKTRYCZNE DODANE LUB PRZENOSZONE
CZARNYM - DO POZOSTAWIENIA

OZNACZENIA

- ŁĄCZNIK POJEDYNCZY
- ŁĄCZNIK PODWÓJNY
- P1_KNX_... PANEL STERUJĄCY OŚWIETLENIEM
- WYPUST OŚWIETLENIOWY SUFITOWY
- WYPUST OŚWIETLENIOWY DLA PUNKTU W SUFICIE G-K
- WYPUST OŚWIETLENIOWY ŚCIENNY
- GNIAZDO ZASILAJĄCE
- GNIAZDO BRYZGOSZCZELNE
- L1 OZNACZENIE POJEDYNCZEJ OPRAWY OŚWIETLENIOWEJ

Nie należy odmierzać wymiarów z rysunku, ani używać go jako szablonu.
Przed zamówieniem i wykonaniem poszczególnych elementów projektu, wszystkie wymiary należy sprawdzić w naturze. W przypadku konieczności podjęcia rozwiązań zastępczych, należy skonsultować się z projektantem. Wszystkie prace należy wykonać zgodnie z obowiązującymi normami, kierując się zasadami wiedzy technicznej, sztuki budowlanej i przepisami, przy zastosowaniu nowoczesnych rozwiązań technicznych i materiałowych. Wszystkie zastosowane materiały muszą posiadać niezbędne certyfikaty i atesty do stosowania w tego typu obiektach.

PROJEKT ARANŻACJI WNĘTRZ DOMU_SW
NAZWA RYSUNKU: **PIĘTRO_PUNKTY ELEKTRYCZNE**

mgr inż. Marta Matusiak, t: 600 093 211.
DOMA PRACOWNIA PROJEKTOWA